

שם הפרויקט: כלניות 17 – טירת הכרמל

2-15 קומה:

אדריכלות

תאריך: 04.12.25

[illegible]

8,13,18,23,28,33,38,43,48,53,58,63,68,73


תאריך	מחלת העדכון

1. סימון אביזרי ריהוט, כלים סניטרים וכדומה הינו להמחשה בלבד. אין להתייחס למידות, צורה וכיוצא'ב, אלא למפרט הטכני בלבד.
2. כל התכניות כפופות לשניוניים עפ"י החלטת הקבלן ו/או יועצי הפרויקט - ייתכנו סטיות בתכניות או במידות.
3. המידות המופיעות בתכניות מתייחסות לחלקי בניין שונים, בין קירות בטון או בניה או גבס, ללא ציפויים מכל סוג שהוא כגון טיח, קרמיקה ועוד. כל המידות הן לאינפורמציה בלבד, אינן סופיות ואינן מחייבות.
4. המידות המדוייקות הן רק מידות שנמדדו באתר בדירה לאחר ביצוע.
5. המידות המחייבות את הקבלן הן אך ורק מידות המופיעות ע"ג תכנית המכר המצורפת לחוזה רכישת הדירה, בסטיות עפ"י דין.

חתימת הדייר על תכנית שינויים זו, מהווה הסכמה מלאה של הדייר לשינויים המופיעים בתכנית זו בלבד.

בזאתו מתו מצויר הדייר כי בדק את התכנית היטב וכי אין לו כל השגות ו/או דרישות נוספות.

תאריך:

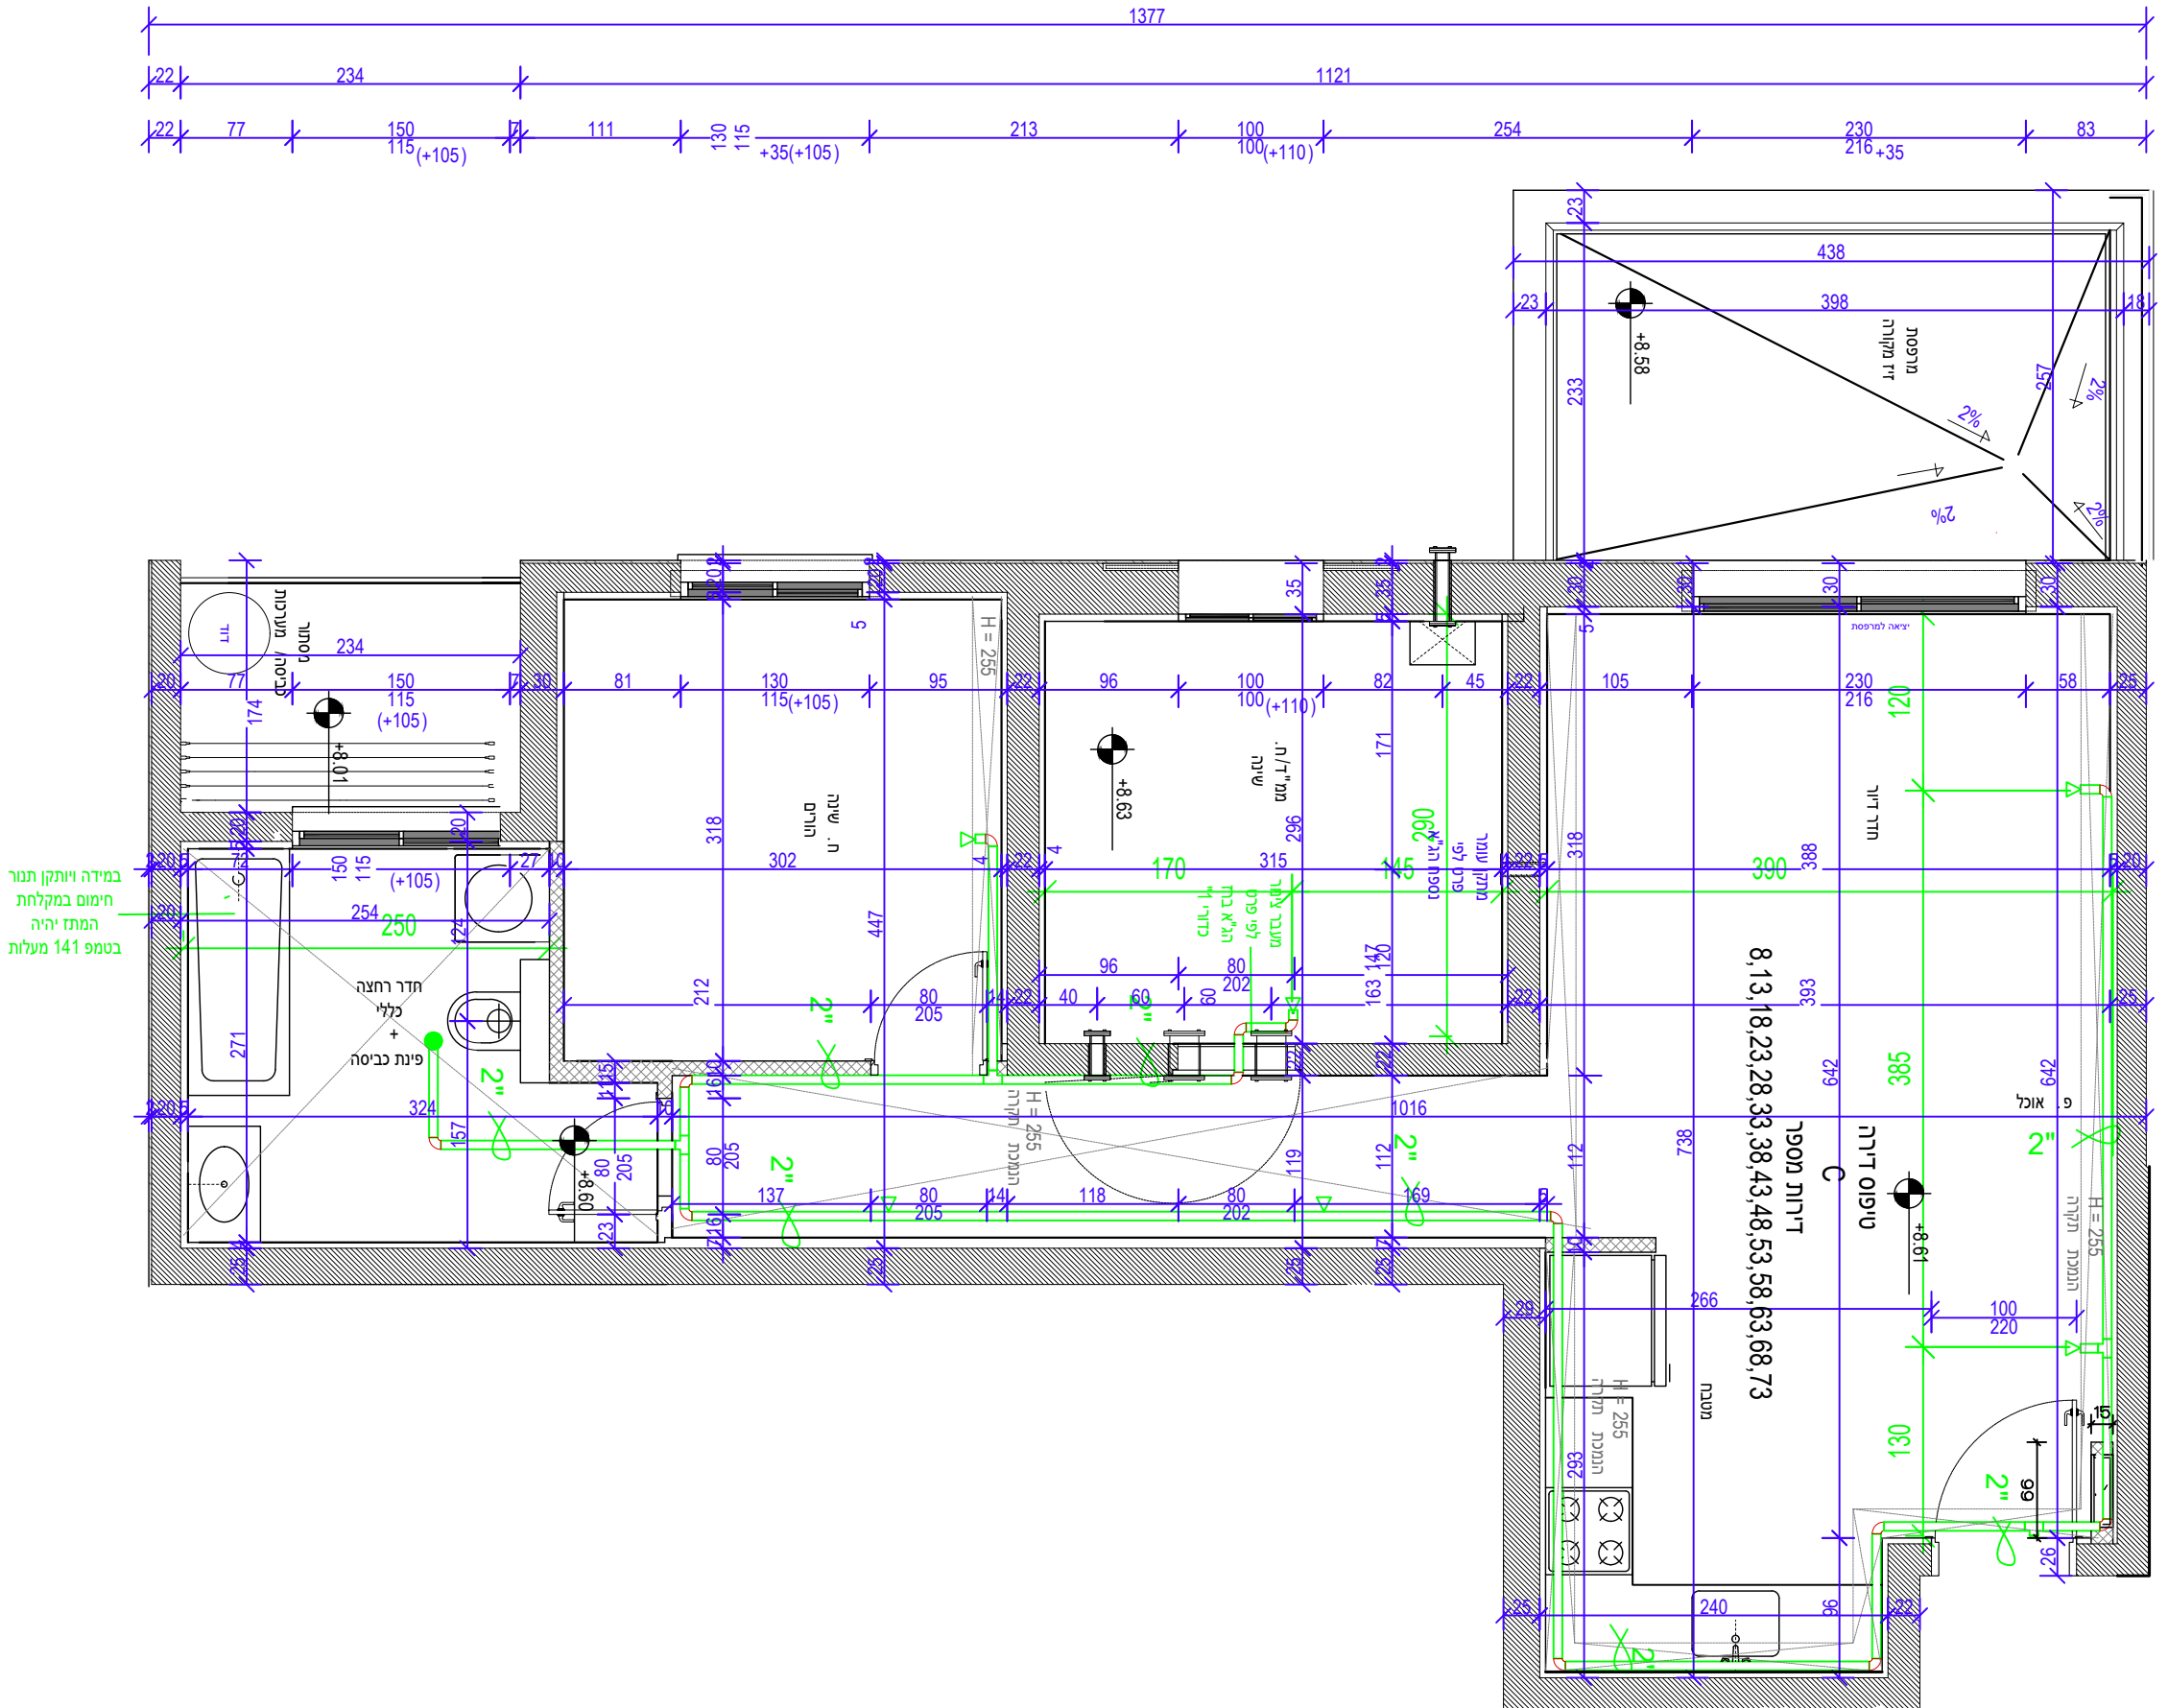

שם הפרויקט: כלניות 17 – טירת הכרמל

מחזורית:	קומה: 2-15	טיפוס: C
מחזורית:	אינסטלציה	שם התכנית:
0	תאריך: 04.12.25	קנ"מ: 150

[illegible]

דירה:


8,13,18,23,28,33,38,43,48,53,58,63,68,73

רשימת עדכונים	
תאריך	מרות העדכון

1. סימון אביזרי ריהוט, כלים סניטרים וכדומה הינו להמחשה בלבד. אין להתייחס למידות, צורה וכיוצ"ב, אלא למפרט הטכני בלבד.
2. כל התכניות כפופות לשינויים ע"י החלטת הקבלן ו/או יועצי הפרויקט - ייתכנו סטיות בתכניות או במידות.
3. המימדות המופיעות בתכניות מתייחסות לחלקי בניין שונים, בין קירות בטון או בניה או גבס, ללא ציפויים מכל סוג שהוא כגון טיח, קרמיקה ועוד. כל המידות הן לאינפורמציה בלבד, אינן סופיות ואינן מחייבות.
4. המידות המדוייקות הן רק מידות שנמדדו באתר בדירה לאחר ביצוע.
5. המימדות המחייבות את הקבלן הן אך ורק מידות המופיעות ע"י תכנית המכר המצורפת לחוזה רכישת הדירה, בסטיות ע"י דין.

חתימת הדייר על תכנית שינויים זו, מהווה הסכמה מלאה של הדייר לשינויים המופיעים בתכנית זו ובלבד.
בחותמתו מצהיר הדייר כי בדק את התכנית היטב וכן אין לו כל השגות ו/או דרישות נוספות.

תאריך:

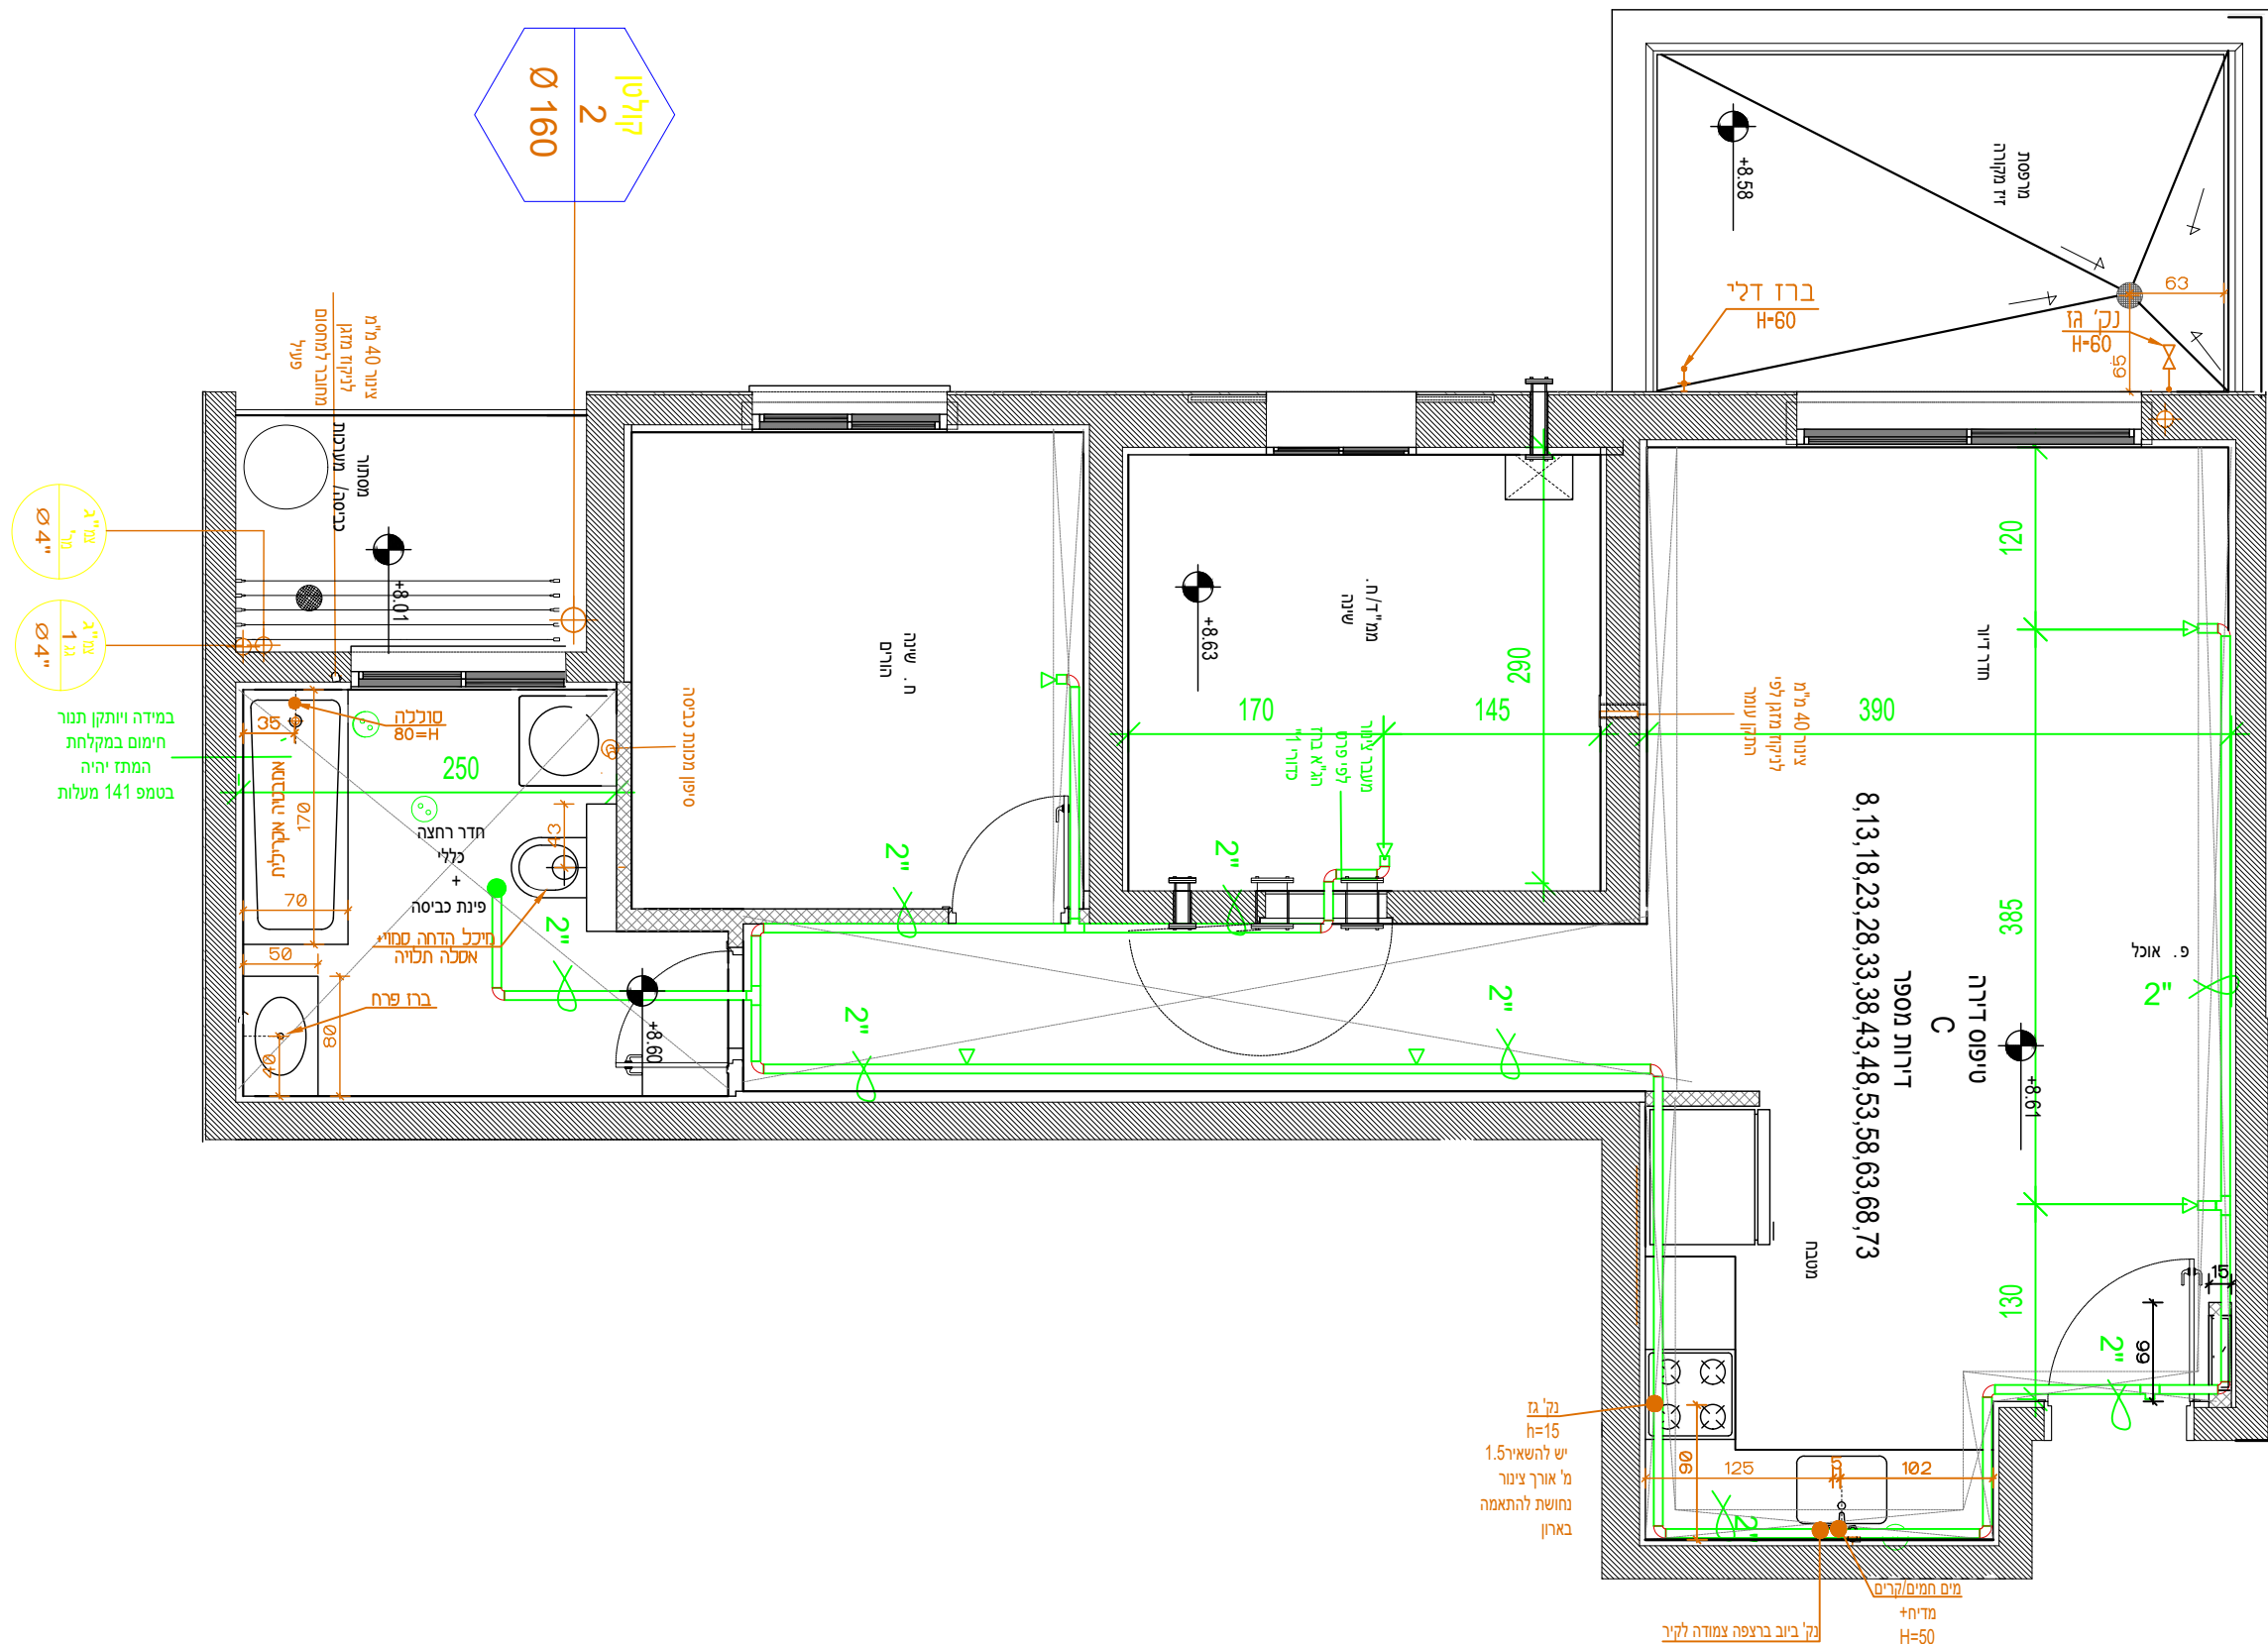

שם הפרויקט: כלניות 17 – טירת הכרמל

טיפוס: C	קומה: 2-15	
שם התכנית: מיזוג איור		
קנ"מ: 150	תאריך: 04.12.25	מהדורה: 0150

[illegible]

דירה:

8,13,18,23,28,33,38,43,48,53,58,63,68,73


רשימת עדכונים	
תאריך	מהות העדכון

1. סימון אביזרי ריהוט, כלים סניטרים וכדומה הינו להמחשה בלבד. אין להתייחס למידות, צורה וכיוצ"ב, אלא למפרט הטכני בלבד.
2. כל התכניות כפופות לשוניים עפי' החלטת הקבלן ו/או יועצי הפרויקט - ייתכנו סטיות בתכניות או במידות.
3. המידות המופיעות בתכניות מתייחסות לחלקי בניין שונים, ביו קירות בטון או בניה או גבס, ללא ציפויים מכל סוג שהוא כגון טיח, קרמיקה ועוד. כל המידות הן לאינפורמציה בלבד, אינן סופיות ואינן מחייבות.
4. המידות המדוייקות הן רק מידות שנמדדו באתר בדירה לאחר ביצוע.
5. המידות המחייבות את הקבלן הן אך ורק מידות המופיעות ע"ג תכנית המכר המצורפת לחוזה רכישת הדירה, בסטיות עפ"י דין.

חתימת הדייר על תכנית שינויים זו, מהווה הסכמה מלאה של הדייר לשינויים המופיעים בתכנית זו בלבד.

בוחתימתי מצהיר הדייר כי בדק את התכנית היטב וכן אין לו כל השגות ו/או דרישות נוספות.

תאריך:

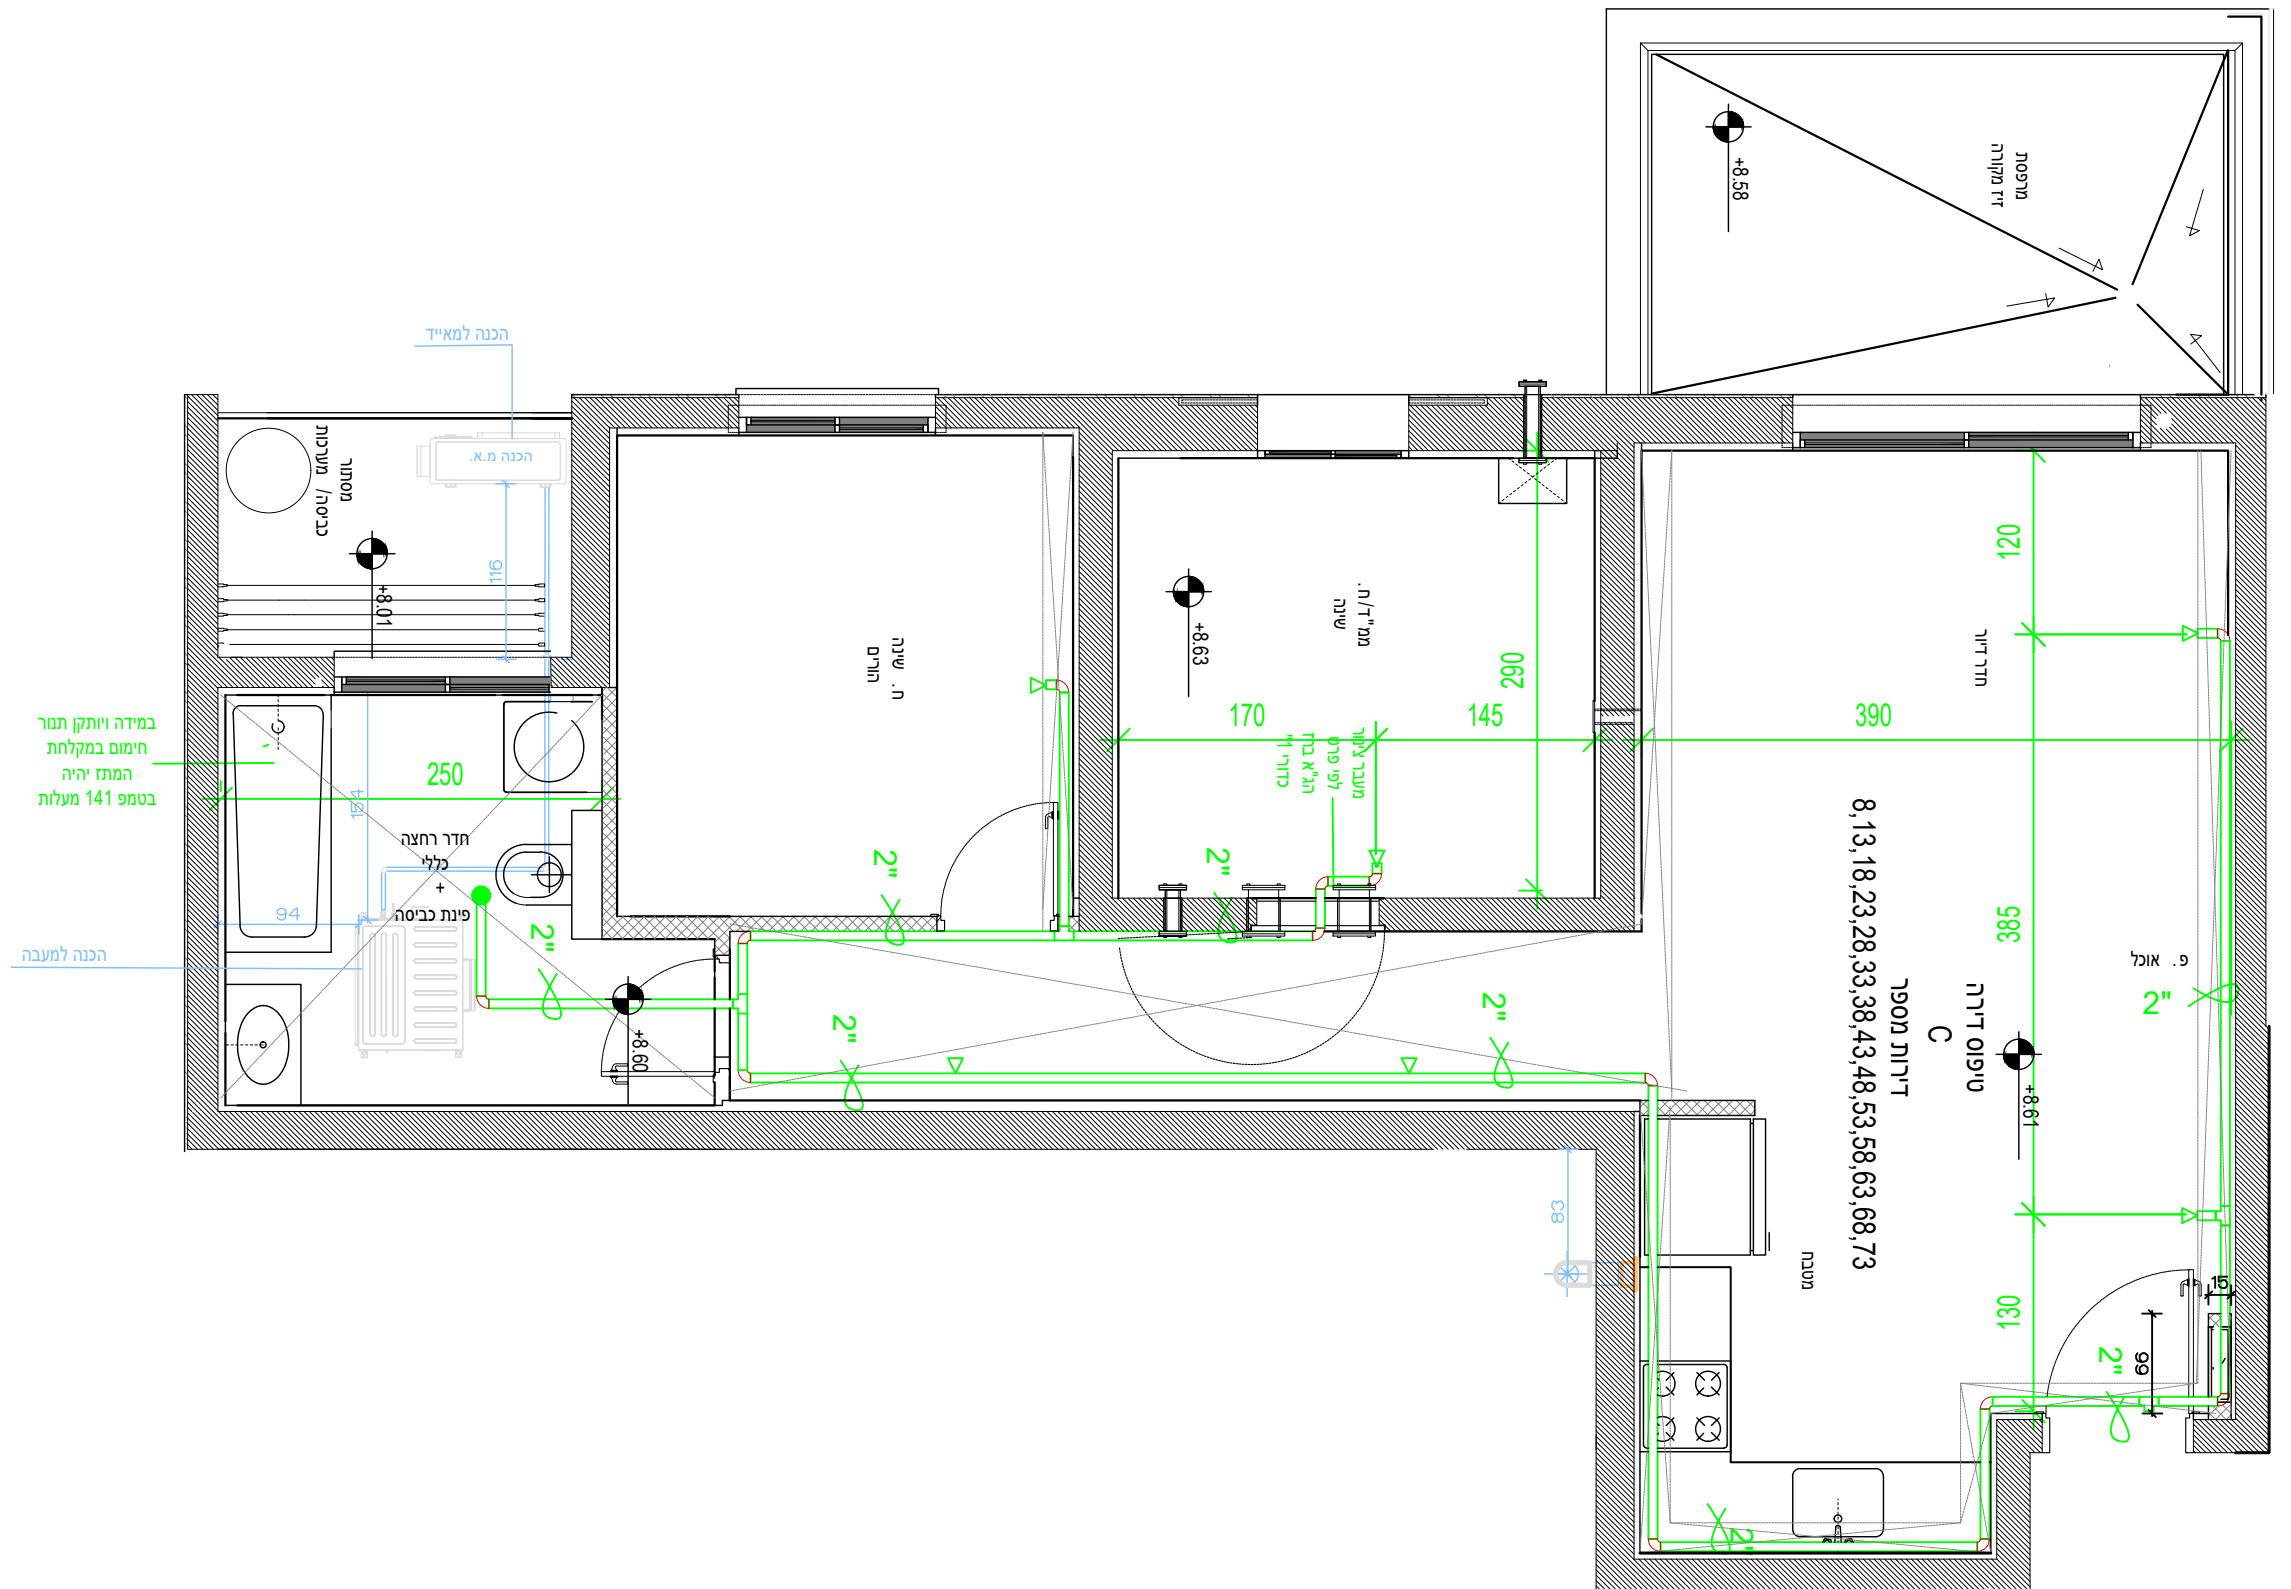

שם הפרויקט: כלניות 17 – טירת הכרמל

	קומה: 2-15	טיפוס: C
מהדורה:	מטבח	שם התכנית:
O	תאריך: 04.12.25	קנ"מ: 150

[illegible]

דירה:


8,13,18,23,28,33,38,43,48,53,58,63,68,73

רשימת עדכונים	
תאריך	מרות העדכון

1. סימון אביזרי ריהוט, כלים סניטרים וכדומה הינו להמחשה בלבד. אין להתייחס למידות, צורה וכיוצ"ב, אלא למפרט הטכני בלבד.
2. כל התכניות כפופות לשוניים עפ"י החלטת הקבלן ו/או יועצי הפרויקט – ייתכנו סטיות בתכניות או במידות.
3. המידות המופיעות בתכניות מתייחסות לחלקי בניין שונים, בין היתר בטון או בניה או גבס, ללא ציפויים מכל סוג שהוא כגון טיח, קרמיקה ועוד. כל המידות הן לאינפורמציה בלבד, אין סופיות ואין מחייבות.
4. המידות המדויקות הן רק מידות שנמדדו באתר בדירה לאחר ביצוע.
5. המידות המחייבות את הקבלן הן אך ורק מידות המופיעות ע"ג תכנית המכר המצורפת לחוזה רכישת הדירה, בסטיות עפ"י דין.

חתימת הדייר על תכנית שינויים זו, מהווה הסכמה מלאה של הדייר לשינויים המופיעים בתכנית זו בלבד.
בחותימתי מצהיר הדייר כי בדק את התכנית היטב וכן אין לו כל השגות ו/או דרישות נוספות.

תאריך:

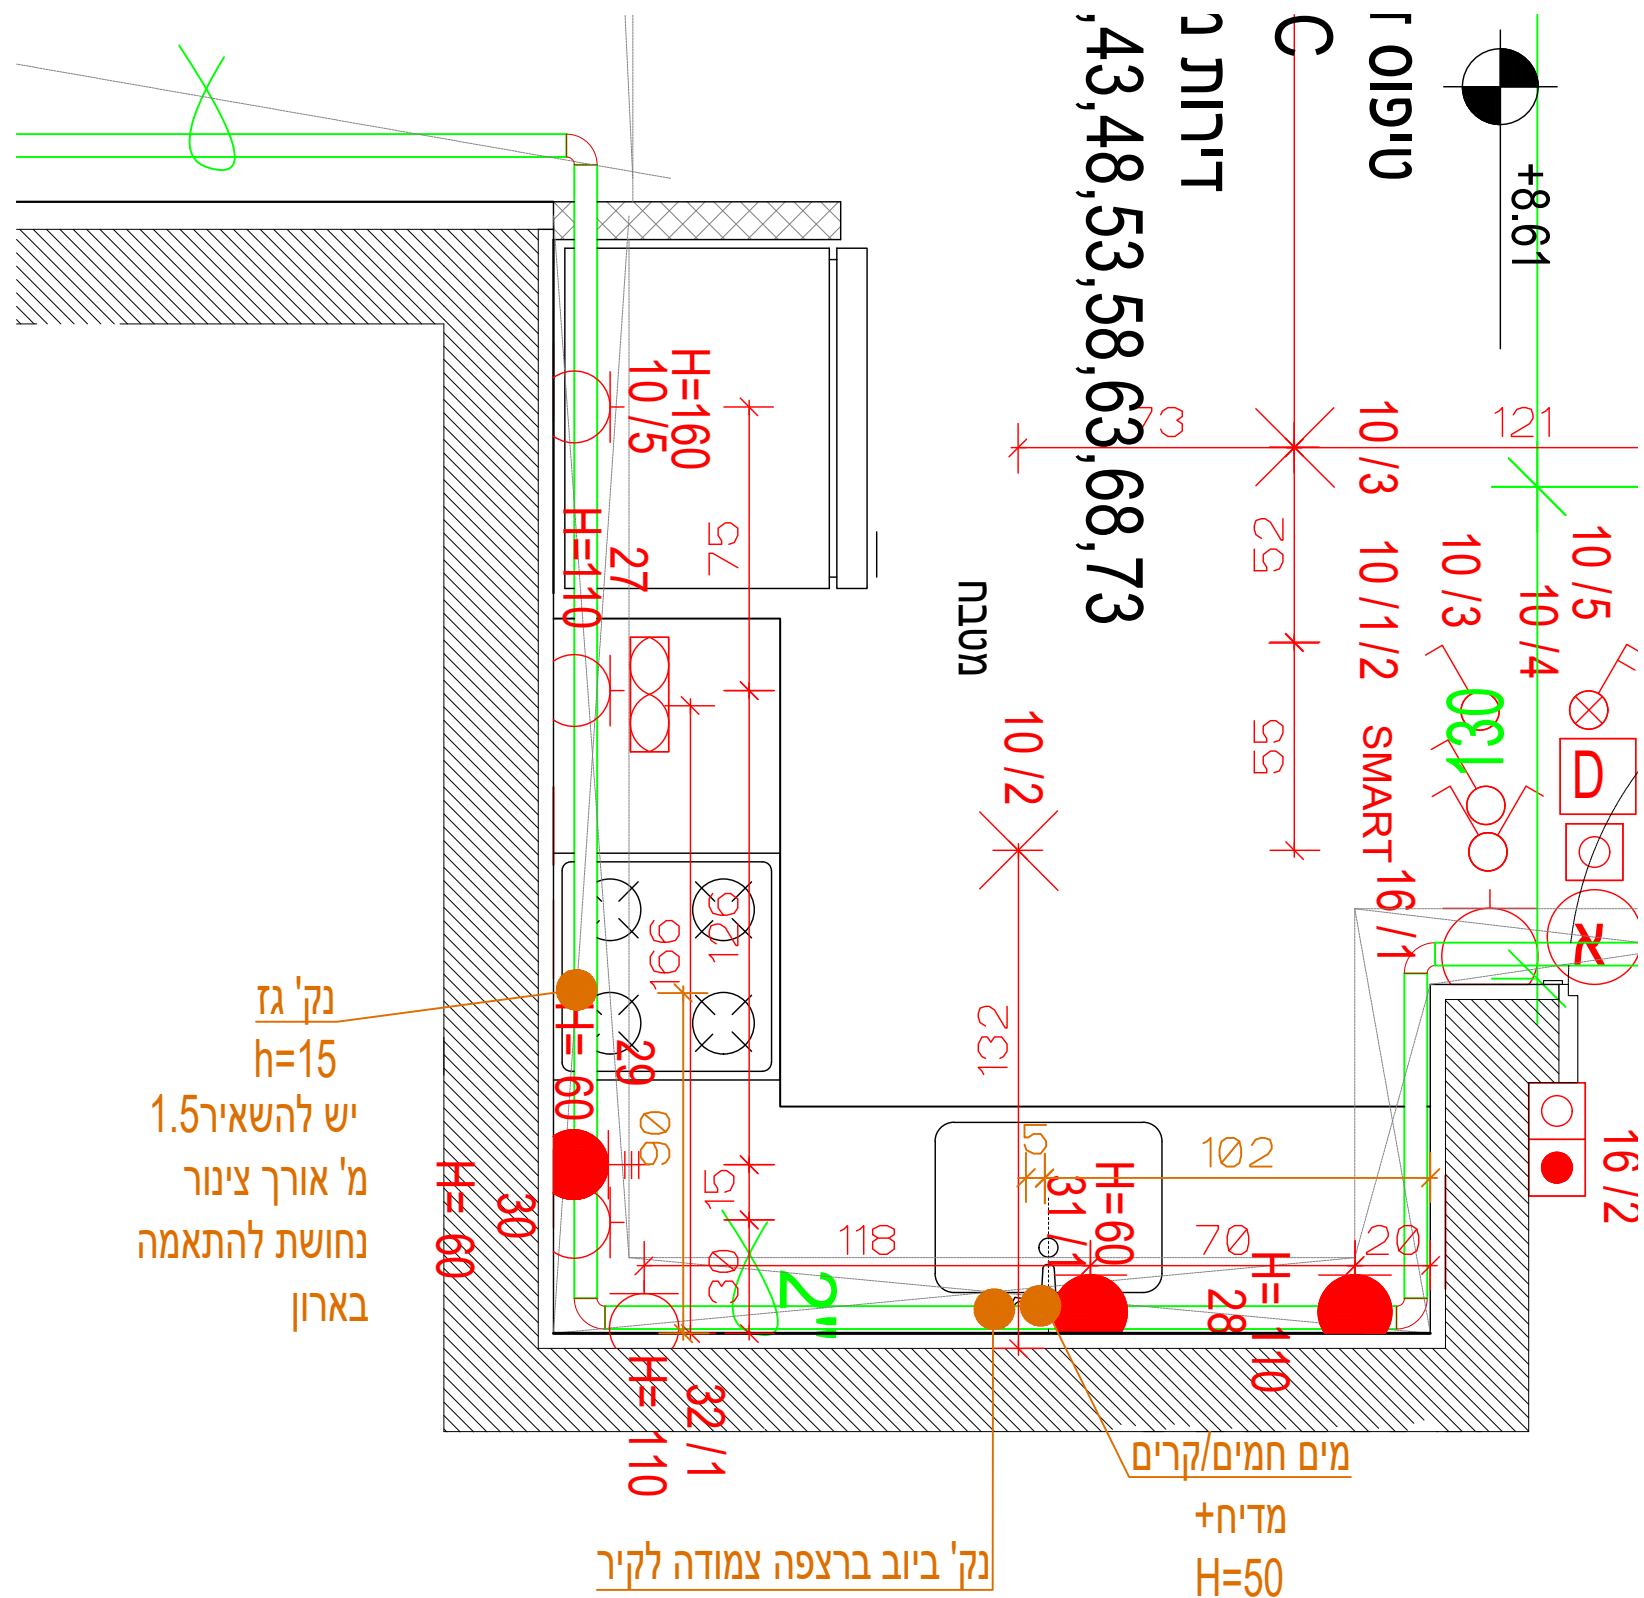

[illegible][illegible]